


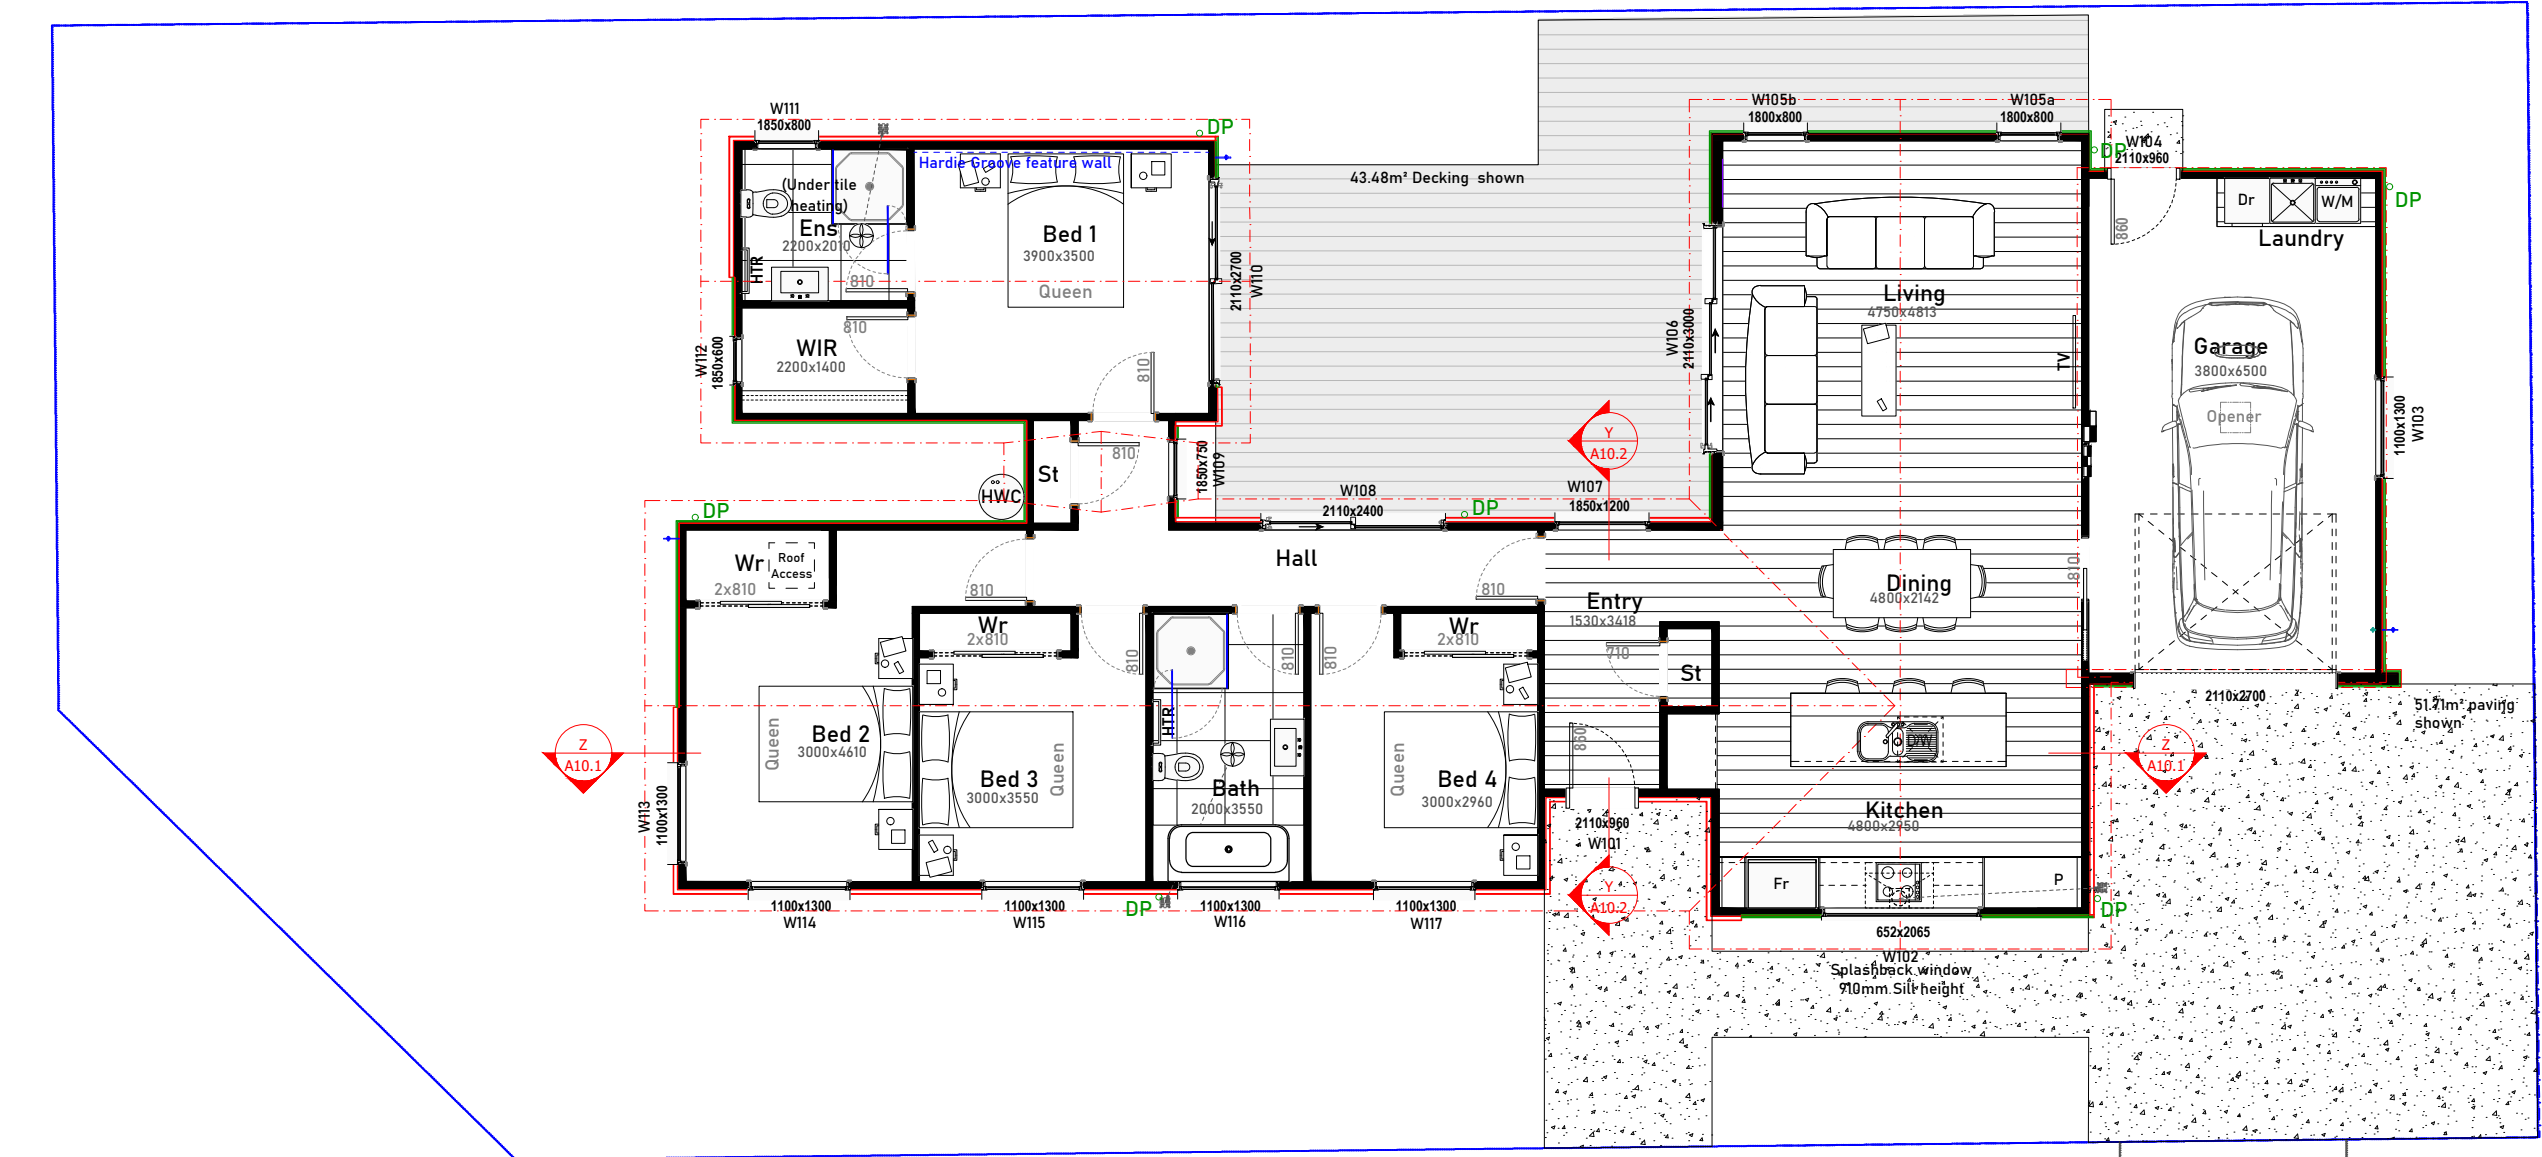

	Floor finished in ceramic tiles.
	Floor finished vinyl plank flooring. Alternative solution applied, see manufacturer's alternative solution statement within A4 Doc's and wall to floor junction detail within details as demonstration of compliance with E3 / AS1 as an alternative solution.
	Exterior paving concrete @ -150mm below FSL at door ways sloping away from foundation, forming compliant access way to building.
	Exterior slatted decking minimum 12mm away from cladding face or door sills. Decking finished height between 0.00 and -0.19 of FFL to provide compliant accessway to building.
	Indicates roof space access hatch, 600x600mm min.
	Indicates hose tap.
	Indicates water toby.
	Indicates meter box.
	Indicates sub board & fibre / data board.
	Indicates 50mm plaster cladding system installed over a 20mm cavity.
	Indicates James Hardie Linea Oblique weatherboard cladding on a 20mm cavity.

JENNIAN HOMES MANAWATU 2013 LTD 275 Broadway Ave, PALMERSTON NORTH	T 06 355 3325
manawatu@jennian.co.nz	www.jennian.co.nz
JENNIAN HOMES MANAWATU 2013 LTD COPYRIGHT: UNDER NO CIRCUMSTANCES SHALL THIS DRAWING BE REPRODUCED WITHOUT PRIOR PERMISSION GIVEN IN WRITING	

DRAWINGS PROVIDED BY:

Jennian
HOMES

Your personality Our expertise

Proposed Dwelling.
Haydon Christian
Lot 33 Awa Park

Issue:	Drawn:	Job Number:	Rev:	Scale:
Consent	Chloe	2567	3	1:100
Sheet name:			Generated:	
Proposed floor plan			3/3/2026	
			Sheet number:	
			A02.01	

Notes:
Standard stud height: 2410mm

All walls lined internally with 10mm Gib board board, stopped to a F4 paint quality finish:
Gib Standard to non wet areas.
Gib Aqualine to wet areas.
Gib Braceline as per bracing plan.

Window sizes on this plan are box unit size, see lintel and uplift fixings plan for trim sizes.

Window sizes are in the format of:
HEIGHT x WIDTH.
All interior door sizes are door leaf sizes.

Internal doors:
Unless otherwise noted internal door height is: 1980mm

Food preparation:
Food preparation surfaces shall be easily maintained in a hygienic condition. Use Stainless steel, decorative high pressure laminate, engineered stone, etc.

Wet areas:
Areas subject to intermittent splash of water around sanitary fittings and appliances such as baths, vanities, laundry tubs, sinks, etc. Are required to have an impervious easily cleaned wall surface adjoining.
At minimum these sheet linings must be finished with one coat of sealer a 2 coats of gloss or semi gloss enamel or acrylic enamel paint.

Where baths, basins, tubs or sinks abut impervious linings, the joint between fixture and lining shall be sealed with wet area MS Sealant to prevent water penetration to concealed spaces or behind linings.

Bathroom shower:	Slateforma
Ensuite shower:	Slateforma

Both with safety glass screens in accordance with: NZS 4223.3 2016.

Areas:

Existing area:	0.00 m²
Proposed area (over frame):	167.24 m²
Proposed area (over foundation):	167.24 m²
Additional coverage area:	2.92 m²

Perimeters:

Perimeter (over frame):	87.44 m
Perimeter (over foundation):	87.44 m

Site conditions:

Wind zone:	High
Earthquake zone:	Zone 3
Corrosion zone:	Zone B
Climate zone:	Zone 3
Snow loading:	N1
Site elevation:	<400
Rainfall intensity:	70

Elevation Key	North Point